


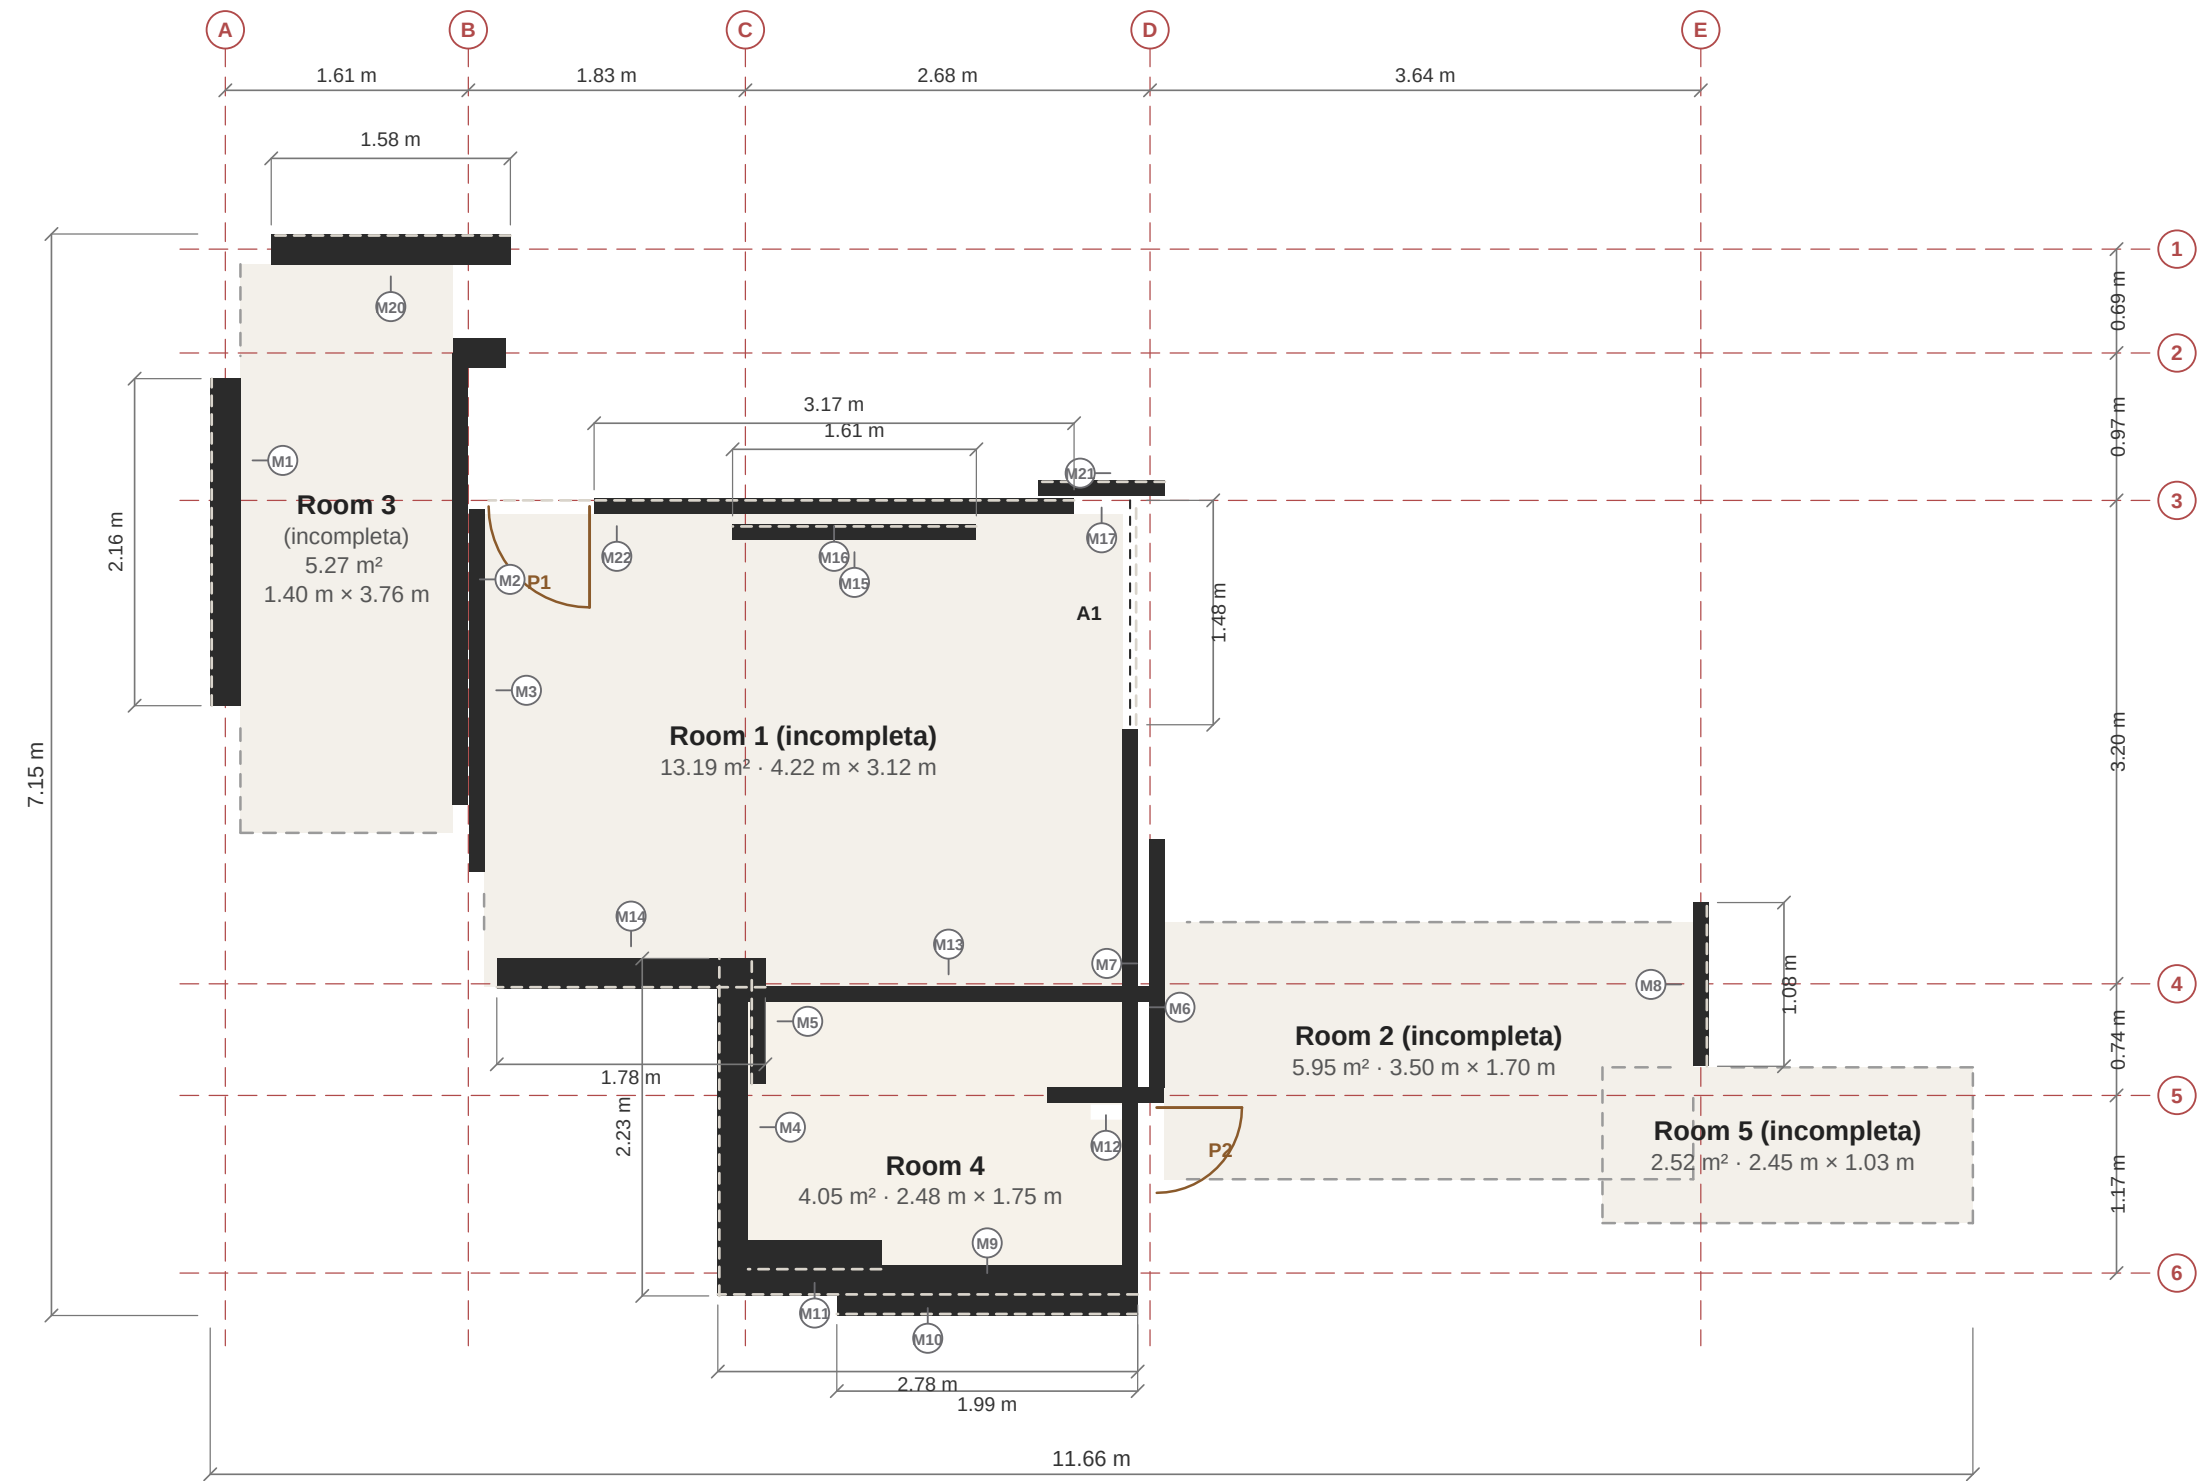

Cuadro de áreas

Nombre	Área	Perímetro
Room 1 *	13.19 m²	14.69 m
Room 2 *	5.95 m²	10.40 m
Room 3 *	5.27 m²	10.33 m
Room 4	4.05 m²	10.95 m
Room 5 *	2.52 m²	6.96 m
Área útil	30.55 m²	
Área de muros	4.86 m²	38.47 m
Área construida	34.92 m²	

* incompleta

Cuadro de carpinterías

Ref.	Tipo	Ancho	H	Antepecho	Muro
P1	puerta	0.67 m	2.05 m	-	M22
P2	puerta	0.56 m	2.05 m	-	M23
A1	paso	1.48 m	3.11 m	-	M21

Notas

- Muros M2, M3, M5, M6, M7, M8, M12, M13, M15, M16, M17, M18, M19, M21, M22, M23: grosor supuesto 0.10 m (vistos por una sola cara).
- Muros M1, M4, M9, M10, M11, M14, M20: grosor supuesto 0.20 m (vistos por una sola cara).
- Room 1, Room 2, Room 3, Room 5: un lado no se escaneó; ahí el contorno sigue el suelo visto.
- La escala viene solo de la red: pasa --focal-px o calibra con --door-width.
- Altura de puerta supuesta (no se vio el dintel): P1, P2.
- No se detectó ninguna ventana. Las ventanas necesitan que se escanee la pared bajo y sobre ellas.
- Escala 1:50: 1:25 no cabe en A3.

PROYECTO

Apartamento U2 (CC BY, YouTube I-JUCu_9xKQ)

Plano: Plano de planta

5 habitaciones · 30.99 m² · techo 3.11 m (medido)

AUTOR

Jhona

Nivel: ±0.00

hecho con levanta

ESCALA

1:50



FECHA

2026-09-05


Rev. A

HOJA


A-01

N: —


Alzados interiores · techo 3.11 m

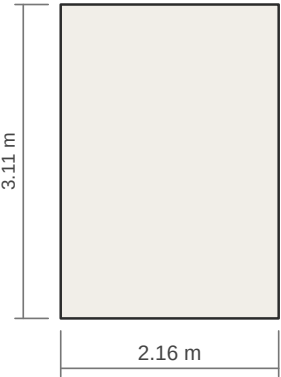


Muro 1 · Room 3
grosor 0.20 m (supuesto)

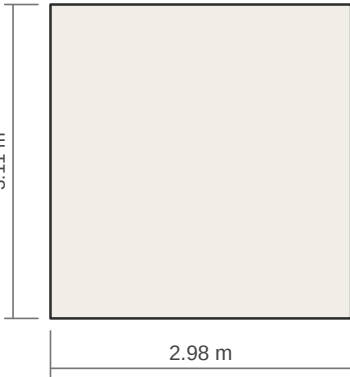

Muro 2 · Room 1
grosor 0.10 m (supuesto)

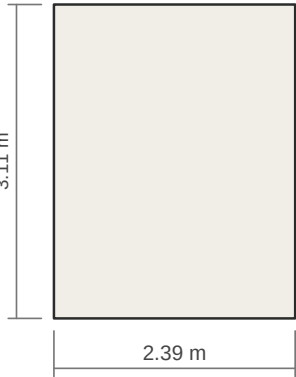


Muro 3 · Room 1
grosor 0.10 m (supuesto)

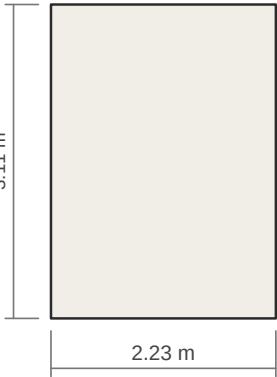


Muro 4 · Room 4
grosor 0.20 m (supuesto)



Muro 5 · Room 4
grosor 0.10 m (supuesto)

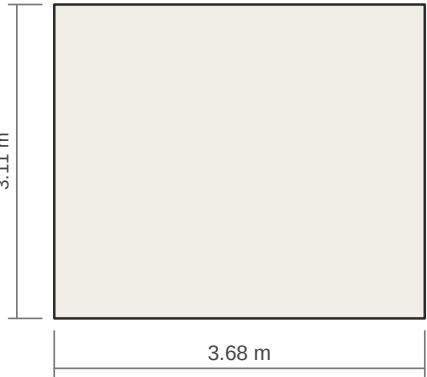


Muro 6 · Room 2
grosor 0.10 m (supuesto)

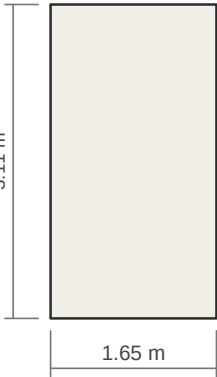


Muro 7 · Room 1
grosor 0.10 m (supuesto)



Muro 8 · Room 2
grosor 0.10 m (supuesto)

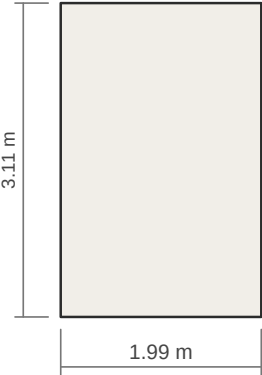

Muro 9 · Room 4
grosor 0.20 m (supuesto)

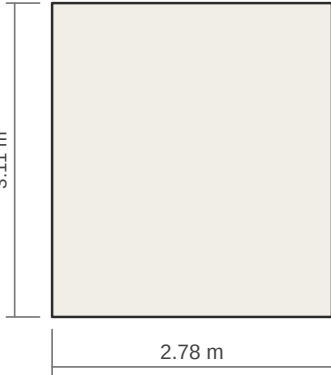


Muro 10 · Room 4
grosor 0.20 m (supuesto)




Muro 11 · Room 4
grosor 0.20 m (supuesto)




Muro 12 · Room 4
grosor 0.10 m (supuesto)

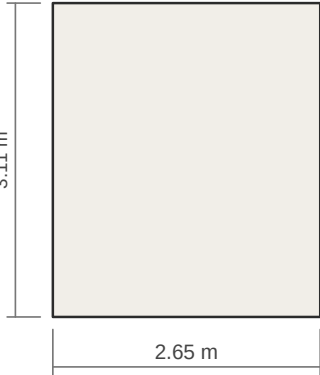


Muro 13 · Room 1
grosor 0.10 m (supuesto)

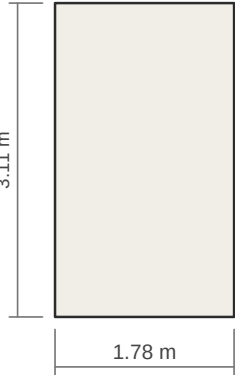

Muro 14 · Room 1
grosor 0.20 m (supuesto)

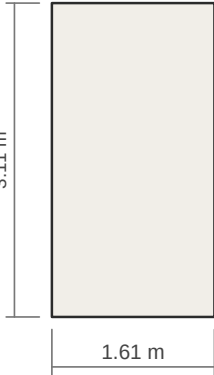


Muro 15 · Room 1
grosor 0.10 m (supuesto)

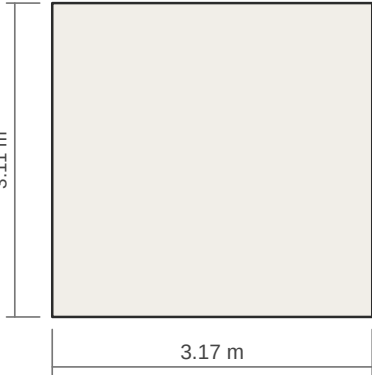


Muro 16 · Room 1
grosor 0.10 m (supuesto)




Muro 17 · Room 1
grosor 0.10 m (supuesto)

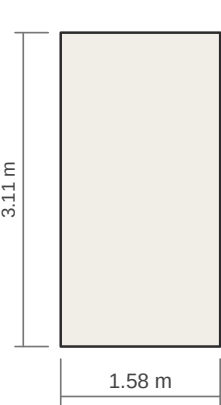

Muro 20 · Room 3
grosor 0.20 m (supuesto)

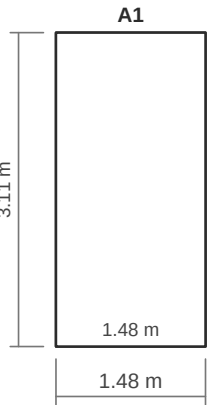

Muro 21 · Room 1
grosor 0.10 m (supuesto)

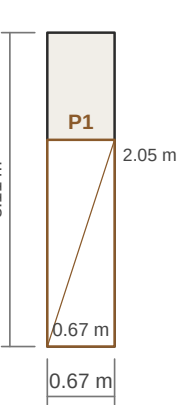

Muro 22 · Room 1
grosor 0.10 m (supuesto)

PROYECTO
Apartamento U2 (CC BY, YouTube I-JUCu_9xKQ)
Plano: Alzados interiores
5 habitaciones · 30.99 m² · techo 3.11 m (medido)

AUTOR
Jhona
Nivel: ±0.00
hecho con levanta

ESCALA
1:75
0 1.00 m

FECHA
2026-09-05
Rev. A

HOJA
A-02
N: —